


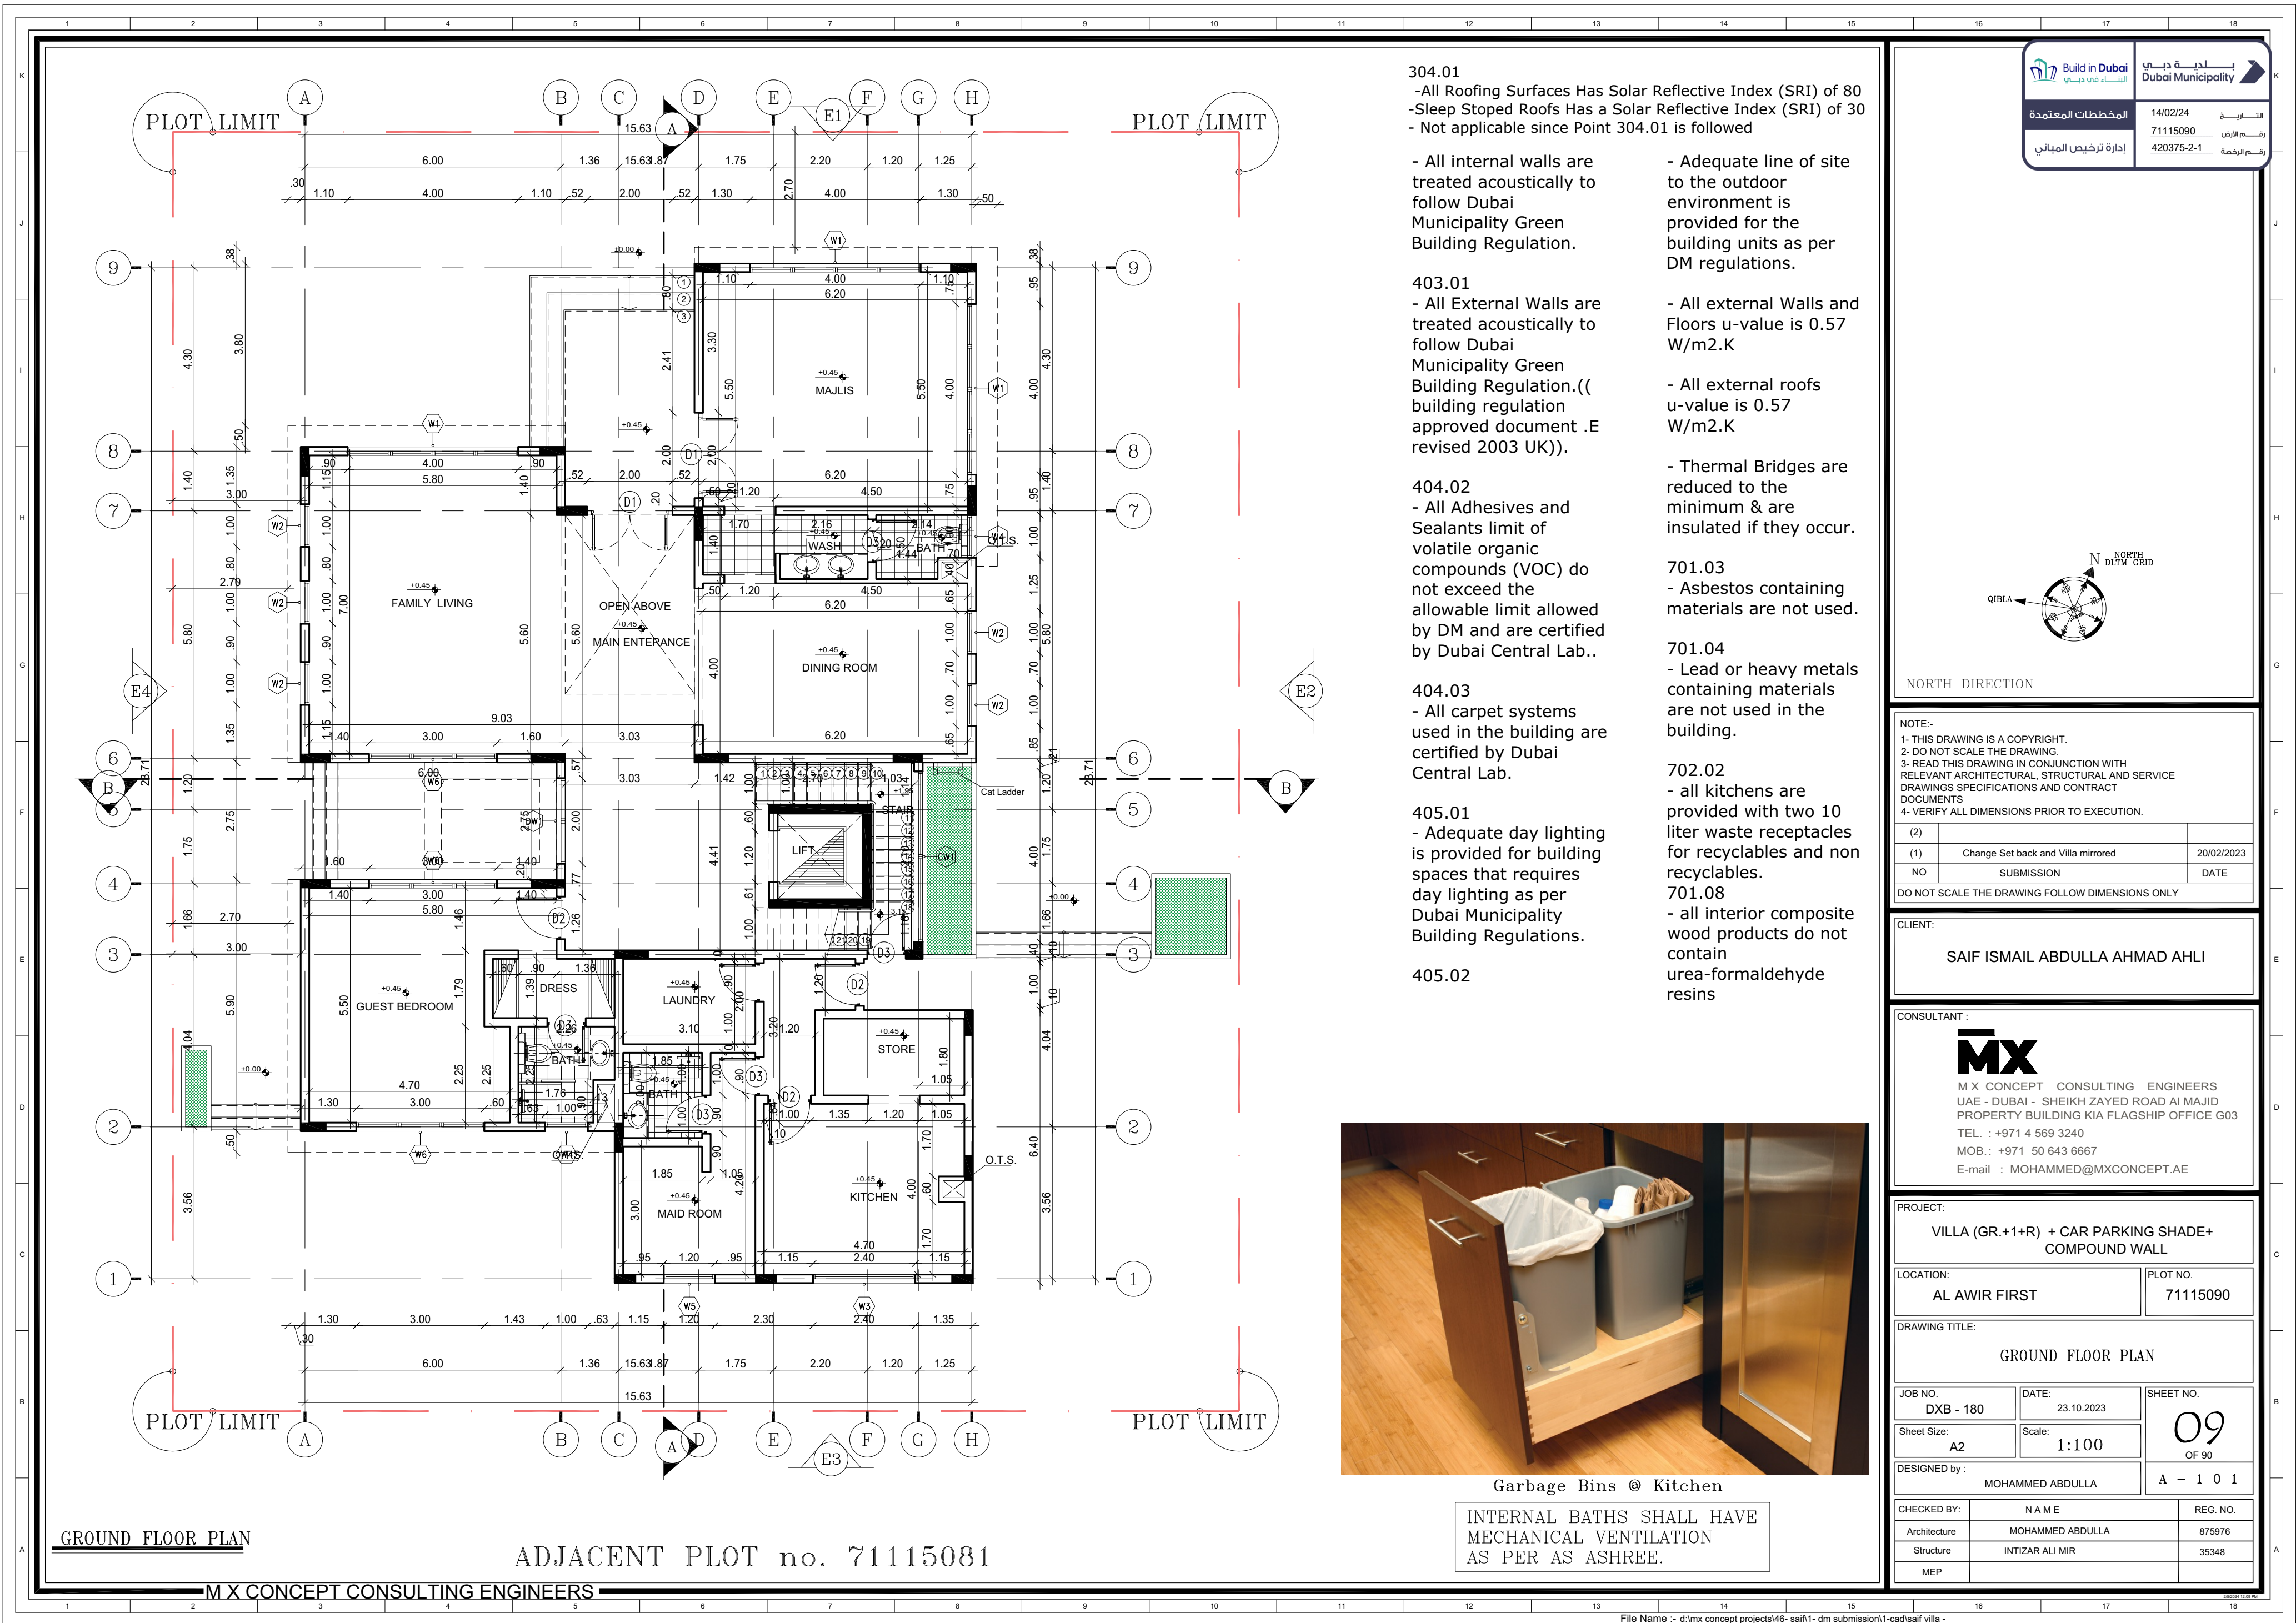

304.01
-All Roofing Surfaces Has Solar Reflective Index (SRI) of 80
-Sleep Stopped Roofs Has a Solar Reflective Index (SRI) of 30
- Not applicable since Point 304.01 is followed

- All internal walls are treated acoustically to follow Dubai Municipality Green Building Regulation.

403.01
- All External Walls are treated acoustically to follow Dubai Municipality Green Building Regulation.((building regulation approved document .E revised 2003 UK)).

404.02
- All Adhesives and Sealants limit of volatile organic compounds (VOC) do not exceed the allowable limit allowed by DM and are certified by Dubai Central Lab..

404.03
- All carpet systems used in the building are certified by Dubai Central Lab.

405.01
- Adequate day lighting is provided for building spaces that requires day lighting as per Dubai Municipality Building Regulations.

405.02

- Adequate line of site to the outdoor environment is provided for the building units as per DM regulations.

- All external Walls and Floors u-value is 0.57 W/m2.K

- All external roofs u-value is 0.57 W/m2.K

- Thermal Bridges are reduced to the minimum & are insulated if they occur.

701.03
- Asbestos containing materials are not used.

701.04
- Lead or heavy metals containing materials are not used in the building.

702.02
- all kitchens are provided with two 10 liter waste receptacles for recyclables and non recyclables.
701.08
- all interior composite wood products do not contain urea-formaldehyde resins



Garbage Bins @ Kitchen


INTERNAL BATHS SHALL HAVE MECHANICAL VENTILATION AS PER AS ASHREE.



المخططات المعتمدة
إدارة ترخيص المباني

بلدية دبي
Dubai Municipality

14/02/24
71115090
420375-2-1

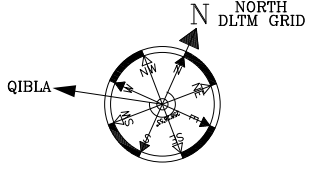

NORTH DIRECTION

NOTE:-
1- THIS DRAWING IS A COPYRIGHT.
2- DO NOT SCALE THE DRAWING.
3- READ THIS DRAWING IN CONJUNCTION WITH RELEVANT ARCHITECTURAL, STRUCTURAL AND SERVICE DRAWINGS SPECIFICATIONS AND CONTRACT DOCUMENTS
4- VERIFY ALL DIMENSIONS PRIOR TO EXECUTION.

(2)		
(1)	Change Set back and Villa mirrored	20/02/2023
NO	SUBMISSION	DATE

DO NOT SCALE THE DRAWING FOLLOW DIMENSIONS ONLY

CLIENT:

SAIF ISMAIL ABDULLA AHMAD AHLI

CONSULTANT :

M X CONCEPT CONSULTING ENGINEERS
UAE - DUBAI - SHEIKH ZAYED ROAD AI MAJID
PROPERTY BUILDING KIA FLAGSHIP OFFICE G03
TEL. : +971 4 569 3240
MOB.: +971 50 643 6667
E-mail : MOHAMMED@MXCONCEPT.AE

PROJECT:
VILLA (GR.+1+R) + CAR PARKING SHADE+ COMPOUND WALL

LOCATION:
AL AWIR FIRST

PLOT NO.
71115090

DRAWING TITLE:
GROUND FLOOR PLAN

JOB NO. DXB - 180	DATE: 23.10.2023	SHEET NO. 09 OF 90
Sheet Size: A2	Scale: 1:100	
DESIGNED by : MOHAMMED ABDULLA		A - 1 0 1


CHECKED BY:	N A M E	REG. NO.
Architecture	MOHAMMED ABDULLA	875976
Structure	INTIZAR ALI MIR	35348
MEP		

GROUND FLOOR PLAN

ADJACENT PLOT no. 71115081

M X CONCEPT CONSULTING ENGINEERS



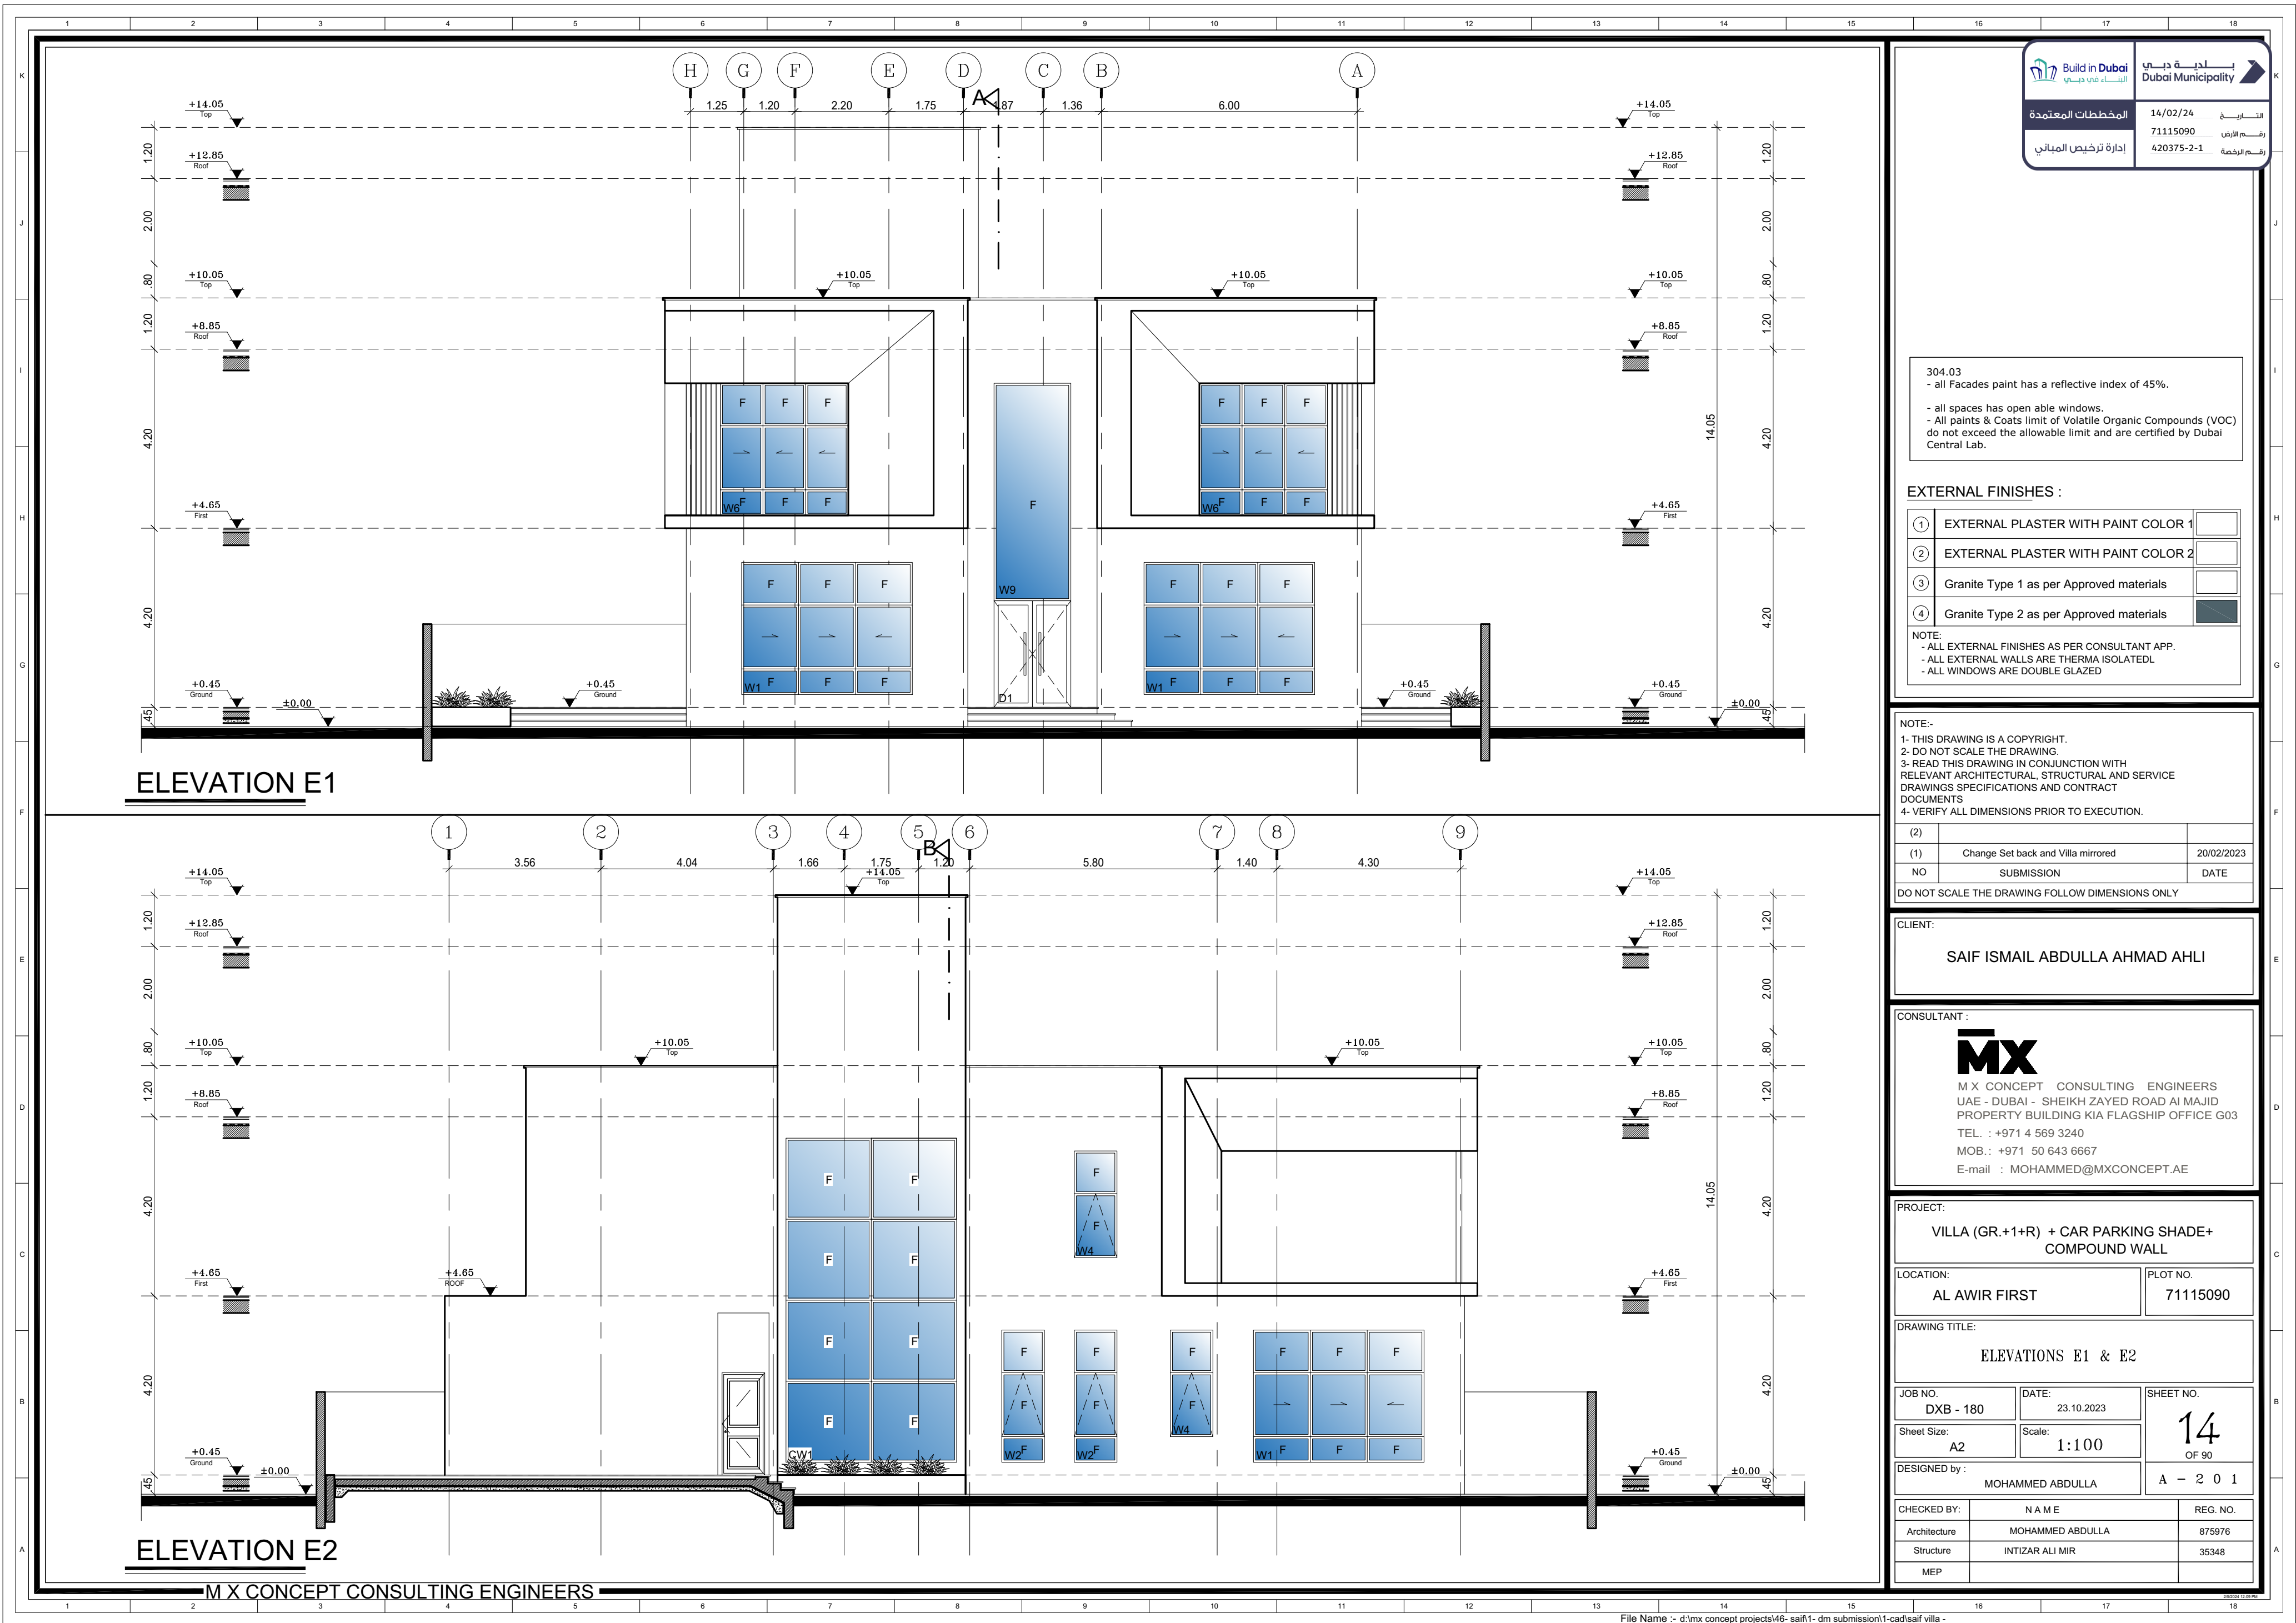



Build in Dubai
البناء في دبي



بلدية دبي
Dubai Municipality

المخططات المعتمدة
إدارة ترخيص المباني

14/02/24
71115090
420375-2-1

التاريخ
رقم الأرض
رقم الرخصة

304.03
- all Facades paint has a reflective index of 45%.

- all spaces has open able windows.
- All paints & Coats limit of Volatile Organic Compounds (VOC) do not exceed the allowable limit and are certified by Dubai Central Lab.

EXTERNAL FINISHES :

1	EXTERNAL PLASTER WITH PAINT COLOR 1	
2	EXTERNAL PLASTER WITH PAINT COLOR 2	
3	Granite Type 1 as per Approved materials	
4	Granite Type 2 as per Approved materials	

NOTE:
- ALL EXTERNAL FINISHES AS PER CONSULTANT APP.
- ALL EXTERNAL WALLS ARE THERMA ISOLATEDL
- ALL WINDOWS ARE DOUBLE GLAZED

NOTE:-
1- THIS DRAWING IS A COPYRIGHT.
2- DO NOT SCALE THE DRAWING.
3- READ THIS DRAWING IN CONJUNCTION WITH RELEVANT ARCHITECTURAL, STRUCTURAL AND SERVICE DRAWINGS SPECIFICATIONS AND CONTRACT DOCUMENTS
4- VERIFY ALL DIMENSIONS PRIOR TO EXECUTION.

(2)		
(1)	Change Set back and Villa mirrored	20/02/2023
NO	SUBMISSION	DATE

DO NOT SCALE THE DRAWING FOLLOW DIMENSIONS ONLY

CLIENT:

SAIF ISMAIL ABDULLA AHMAD AHLI

CONSULTANT :

MX

M X CONCEPT CONSULTING ENGINEERS
UAE - DUBAI - SHEIKH ZAYED ROAD AI MAJID
PROPERTY BUILDING KIA FLAGSHIP OFFICE G03
TEL. : +971 4 569 3240
MOB.: +971 50 643 6667
E-mail : MOHAMMED@MXCONCEPT.AE

PROJECT:

VILLA (GR.+1+R) + CAR PARKING SHADE+ COMPOUND WALL

LOCATION: AL AWIR FIRST

PLOT NO. 71115090

DRAWING TITLE:

ELEVATIONS E1 & E2

JOB NO. DXB - 180	DATE: 23.10.2023	SHEET NO. 14 OF 90
Sheet Size: A2	Scale: 1:100	DESIGNED by : MOHAMMED ABDULLA
CHECKED BY: N A M E		REG. NO.
Architecture MOHAMMED ABDULLA		875976
Structure INTIZAR ALI MIR		35348
MEP		

304.03
- all Facades paint has a reflective index of 45%.

- all spaces has open able windows.
- All paints & Coats limit of Volatile Organic Compounds (VOC) do not exceed the allowable limit and are certified by Dubai Central Lab.

EXTERNAL FINISHES :

1	EXTERNAL PLASTER WITH PAINT COLOR 1	
2	EXTERNAL PLASTER WITH PAINT COLOR 2	
3	Granite Type 1 as per Approved materials	
4	Granite Type 2 as per Approved materials	

NOTE:
- ALL EXTERNAL FINISHES AS PER CONSULTANT APP.
- ALL EXTERNAL WALLS ARE THERMA ISOLATEDL
- ALL WINDOWS ARE DOUBLE GLAZED

NOTE:-
1- THIS DRAWING IS A COPYRIGHT.
2- DO NOT SCALE THE DRAWING.
3- READ THIS DRAWING IN CONJUNCTION WITH RELEVANT ARCHITECTURAL, STRUCTURAL AND SERVICE DRAWINGS SPECIFICATIONS AND CONTRACT DOCUMENTS
4- VERIFY ALL DIMENSIONS PRIOR TO EXECUTION.

(2)		
(1)	Change Set back and Villa mirrored	20/02/2023
NO	SUBMISSION	DATE

DO NOT SCALE THE DRAWING FOLLOW DIMENSIONS ONLY

CLIENT:

SAIF ISMAIL ABDULLA AHMAD AHLI

CONSULTANT :



M X CONCEPT CONSULTING ENGINEERS
UAE - DUBAI - SHEIKH ZAYED ROAD AI MAJID
PROPERTY BUILDING KIA FLAGSHIP OFFICE G03
TEL. : +971 4 569 3240
MOB.: +971 50 643 6667
E-mail : MOHAMMED@MXCONCEPT.AE

PROJECT:

VILLA (GR.+1+R) + CAR PARKING SHADE+
COMPOUND WALL

LOCATION:

AL AWIR FIRST

PLOT NO.

71115090

DRAWING TITLE:

ELEVATIONS E3 & E4

JOB NO.

DXB - 180

DATE:

23.10.2023

SHEET NO.

15

Sheet Size:

A2

Scale:

1:100

OF 90

DESIGNED by :

MOHAMMED ABDULLA

A - 2 0 2

CHECKED BY:

N A M E

REG. NO.

Architecture MOHAMMED ABDULLA

875976

Structure INTIZAR ALI MIR

35348

MEP

ELEVATION E3

ELEVATION E4

M X CONCEPT CONSULTING ENGINEERS

304.03
- all Facades paint has a reflective index of 45%.

- all spaces has open able windows.
- All paints & Coats limit of Volatile Organic Compounds (VOC) do not exceed the allowable limit and are certified by Dubai Central Lab.

EXTERNAL FINISHES :

1	EXTERNAL PLASTER WITH PAINT COLOR 1	
2	EXTERNAL PLASTER WITH PAINT COLOR 2	
3	Granite Type 1 as per Approved materials	
4	Granite Type 2 as per Approved materials	

NOTE:
- ALL EXTERNAL FINISHES AS PER CONSULTANT APP.
- ALL EXTERNAL WALLS ARE THERMA ISOLATEDL
- ALL WINDOWS ARE DOUBLE GLAZED

NOTE:-
1- THIS DRAWING IS A COPYRIGHT.
2- DO NOT SCALE THE DRAWING.
3- READ THIS DRAWING IN CONJUNCTION WITH RELEVANT ARCHITECTURAL, STRUCTURAL AND SERVICE DRAWINGS SPECIFICATIONS AND CONTRACT DOCUMENTS
4- VERIFY ALL DIMENSIONS PRIOR TO EXECUTION.

(2)		
(1)	Change Set back and Villa mirrored	20/02/2023
NO	SUBMISSION	DATE

DO NOT SCALE THE DRAWING FOLLOW DIMENSIONS ONLY

CLIENT:

SAIF ISMAIL ABDULLA AHMAD AHLI

CONSULTANT :

MX

M X CONCEPT CONSULTING ENGINEERS
UAE - DUBAI - SHEIKH ZAYED ROAD AI MAJID
PROPERTY BUILDING KIA FLAGSHIP OFFICE G03
TEL. : +971 4 569 3240
MOB.: +971 50 643 6667
E-mail : MOHAMMED@MXCONCEPT.AE

PROJECT:

VILLA (GR.+1+R) + CAR PARKING SHADE+
COMPOUND WALL

LOCATION:

AL AWIR FIRST

PLOT NO.

71115090

DRAWING TITLE:

SECTION A-A & B-B

JOB NO.

DXB - 180

DATE:

23.10.2023

SHEET NO.

16

Sheet Size:

A2

Scale:

1:100

OF 90

DESIGNED by :

MOHAMMED ABDULLA

A - 3 0 1

CHECKED BY:

N A M E

REG. NO.

Architecture

MOHAMMED ABDULLA

875976


Structure

INTIZAR ALI MIR

35348


MEP

SECTION A-A

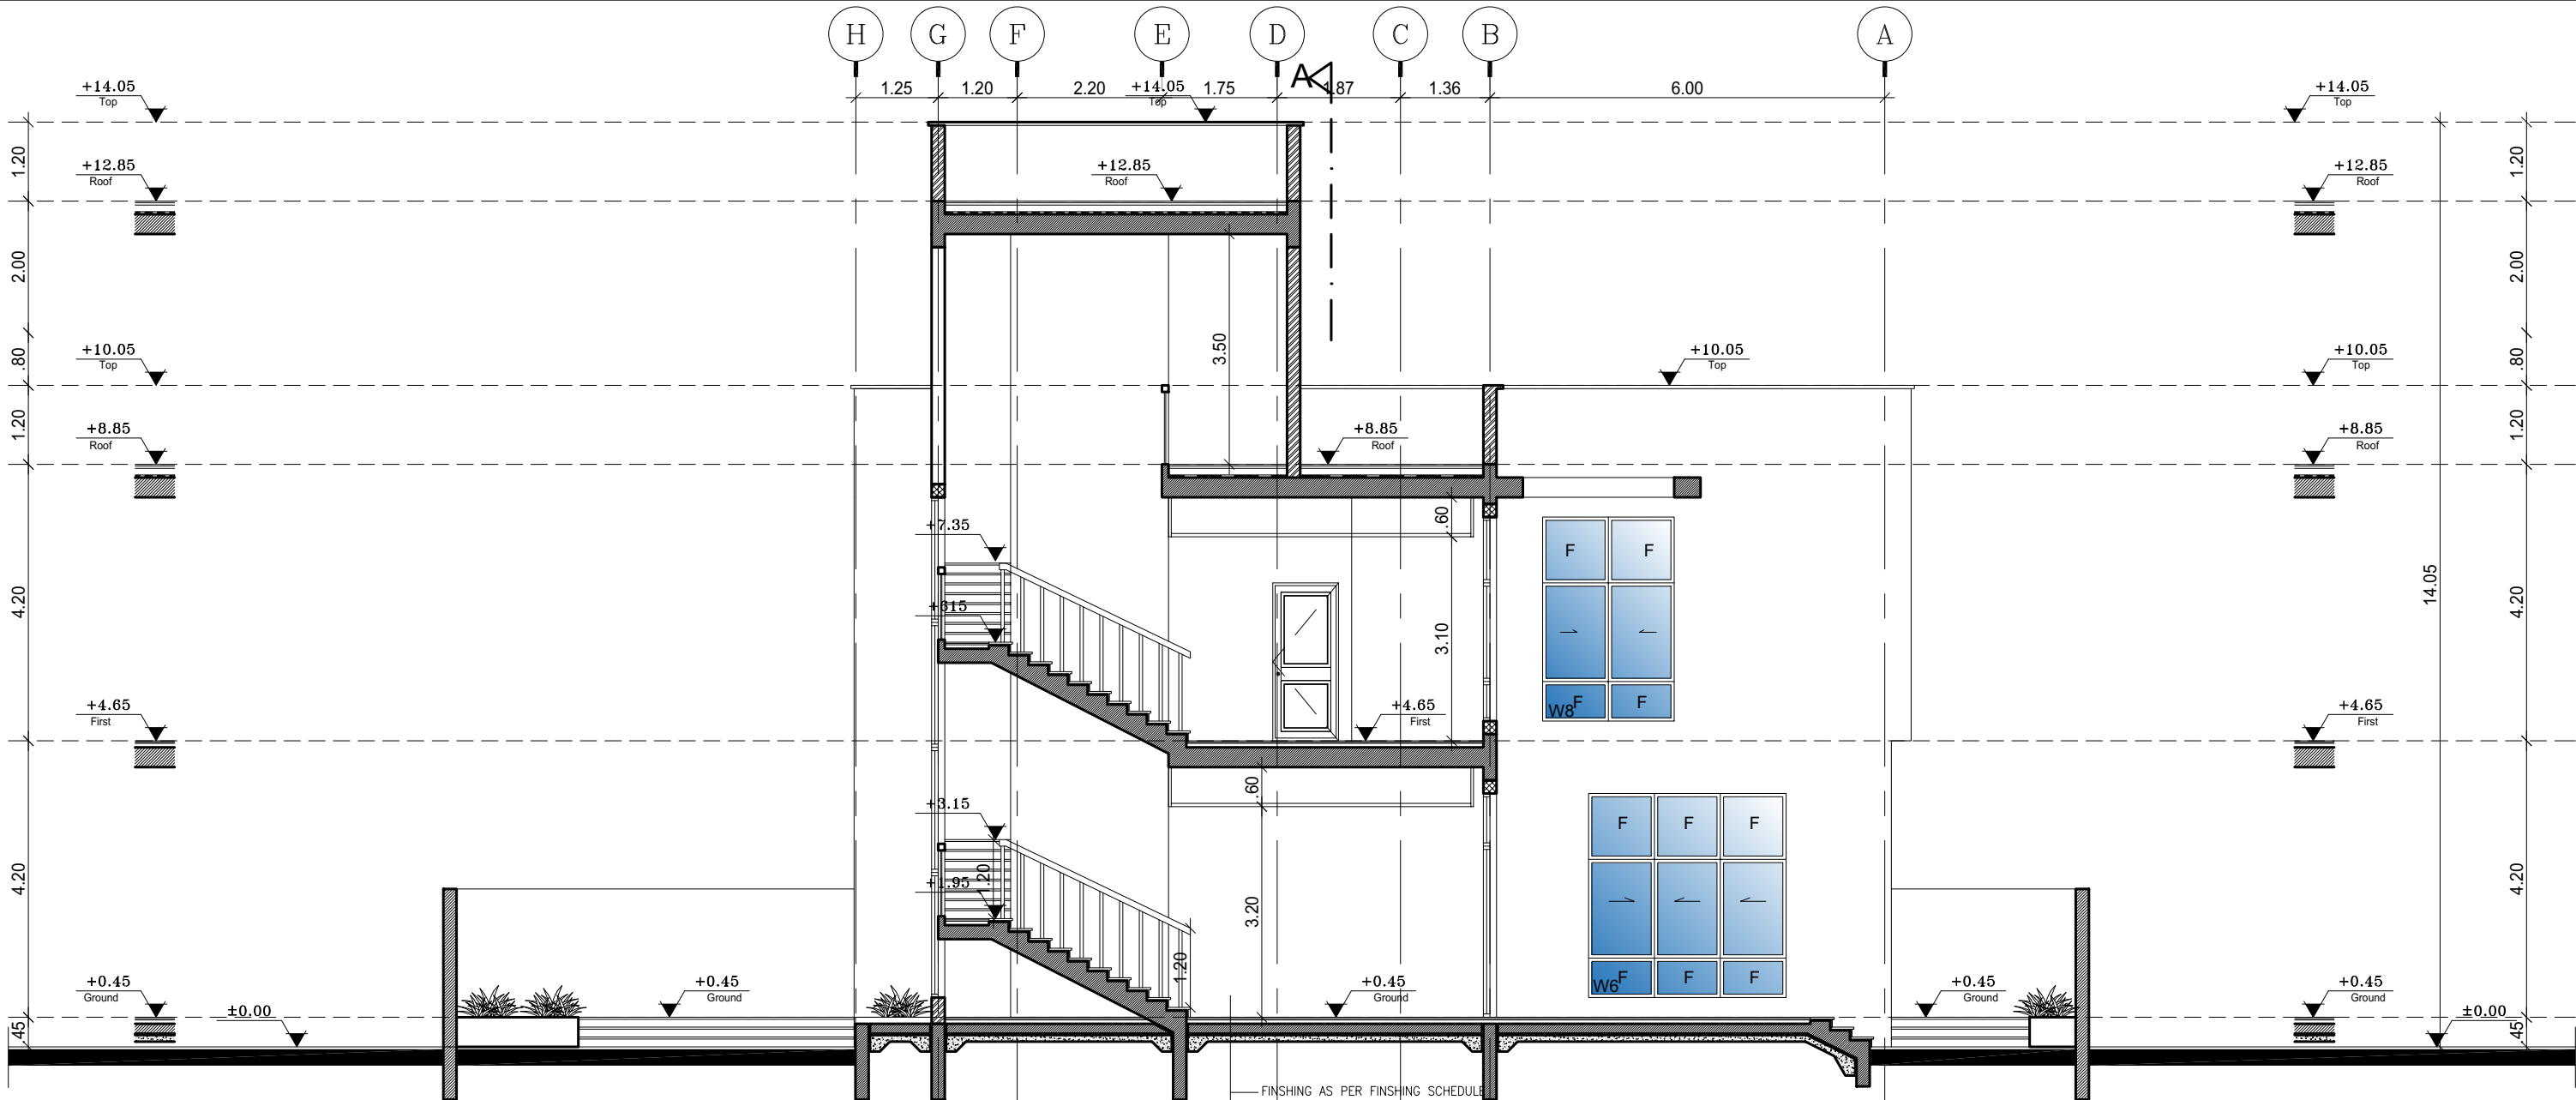

SECTION B-B

M X CONCEPT CONSULTING ENGINEERS

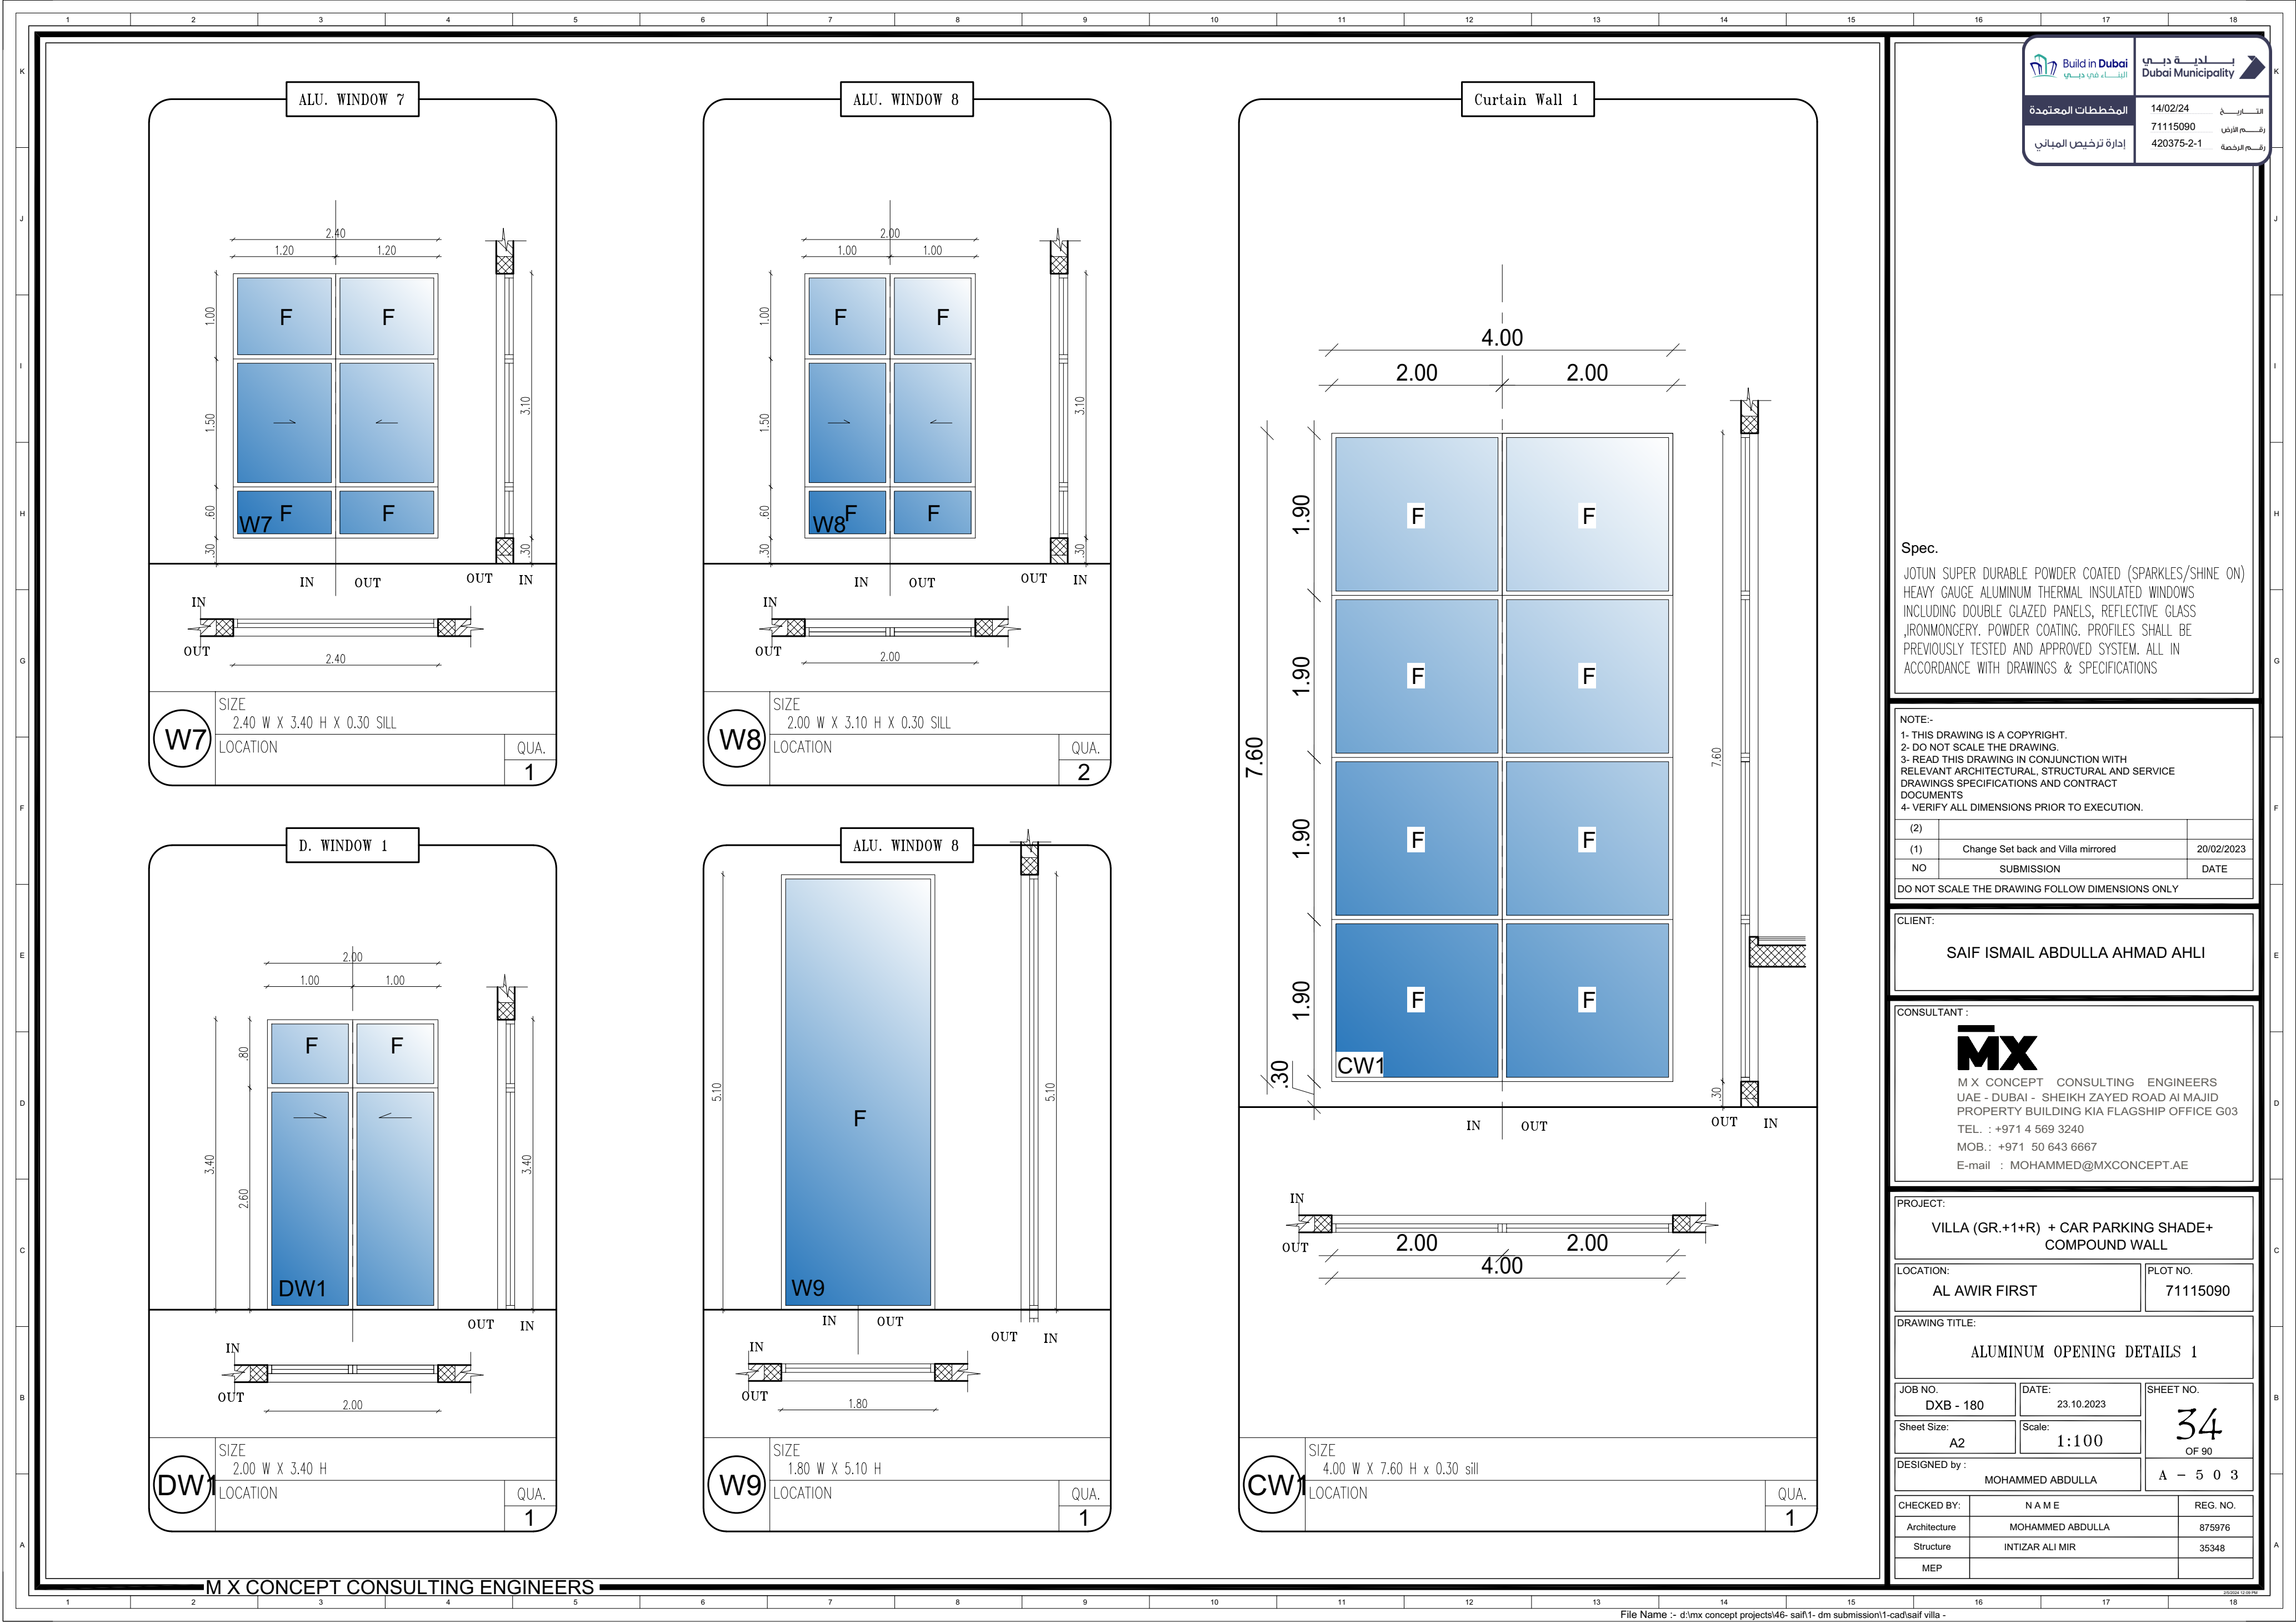



Build in Dubai
البناء في دبي



بلدية دبي
Dubai Municipality

المخططات المعتمدة

إدارة ترخيص المباني

التاريخ
14/02/24

رقم الأرض
71115090

رقم الرخصة
420375-2-1

Spec.

JOTUN SUPER DURABLE POWDER COATED (SPARKLES/SHINE ON) HEAVY GAUGE ALUMINUM THERMAL INSULATED WINDOWS INCLUDING DOUBLE GLAZED PANELS, REFLECTIVE GLASS ,IRONMONGERY. POWDER COATING. PROFILES SHALL BE PREVIOUSLY TESTED AND APPROVED SYSTEM. ALL IN ACCORDANCE WITH DRAWINGS & SPECIFICATIONS

NOTE:-

- 1- THIS DRAWING IS A COPYRIGHT.
- 2- DO NOT SCALE THE DRAWING.
- 3- READ THIS DRAWING IN CONJUNCTION WITH RELEVANT ARCHITECTURAL, STRUCTURAL AND SERVICE DRAWINGS SPECIFICATIONS AND CONTRACT DOCUMENTS
- 4- VERIFY ALL DIMENSIONS PRIOR TO EXECUTION.

(2)		
(1)	Change Set back and Villa mirrored	20/02/2023
NO	SUBMISSION	DATE

DO NOT SCALE THE DRAWING FOLLOW DIMENSIONS ONLY

CLIENT:

SAIF ISMAIL ABDULLA AHMAD AHLI

CONSULTANT :



M X CONCEPT CONSULTING ENGINEERS
UAE - DUBAI - SHEIKH ZAYED ROAD AI MAJID
PROPERTY BUILDING KIA FLAGSHIP OFFICE G03
TEL. : +971 4 569 3240
MOB.: +971 50 643 6667
E-mail : MOHAMMED@MXCONCEPT.AE

PROJECT: VILLA (GR.+1+R) + CAR PARKING SHADE+ COMPOUND WALL		
LOCATION: AL AWIR FIRST	PLOT NO. 71115090	
DRAWING TITLE: ALUMINUM OPENING DETAILS 1		
JOB NO. DXB - 180	DATE: 23.10.2023	SHEET NO. 34 OF 90
Sheet Size: A2	Scale: 1:100	
DESIGNED by : MOHAMMED ABDULLA		A - 5 0 3
CHECKED BY:	N A M E	REG. NO.
Architecture	MOHAMMED ABDULLA	875976
Structure	INTIZAR ALI MIR	35348
MEP		

